


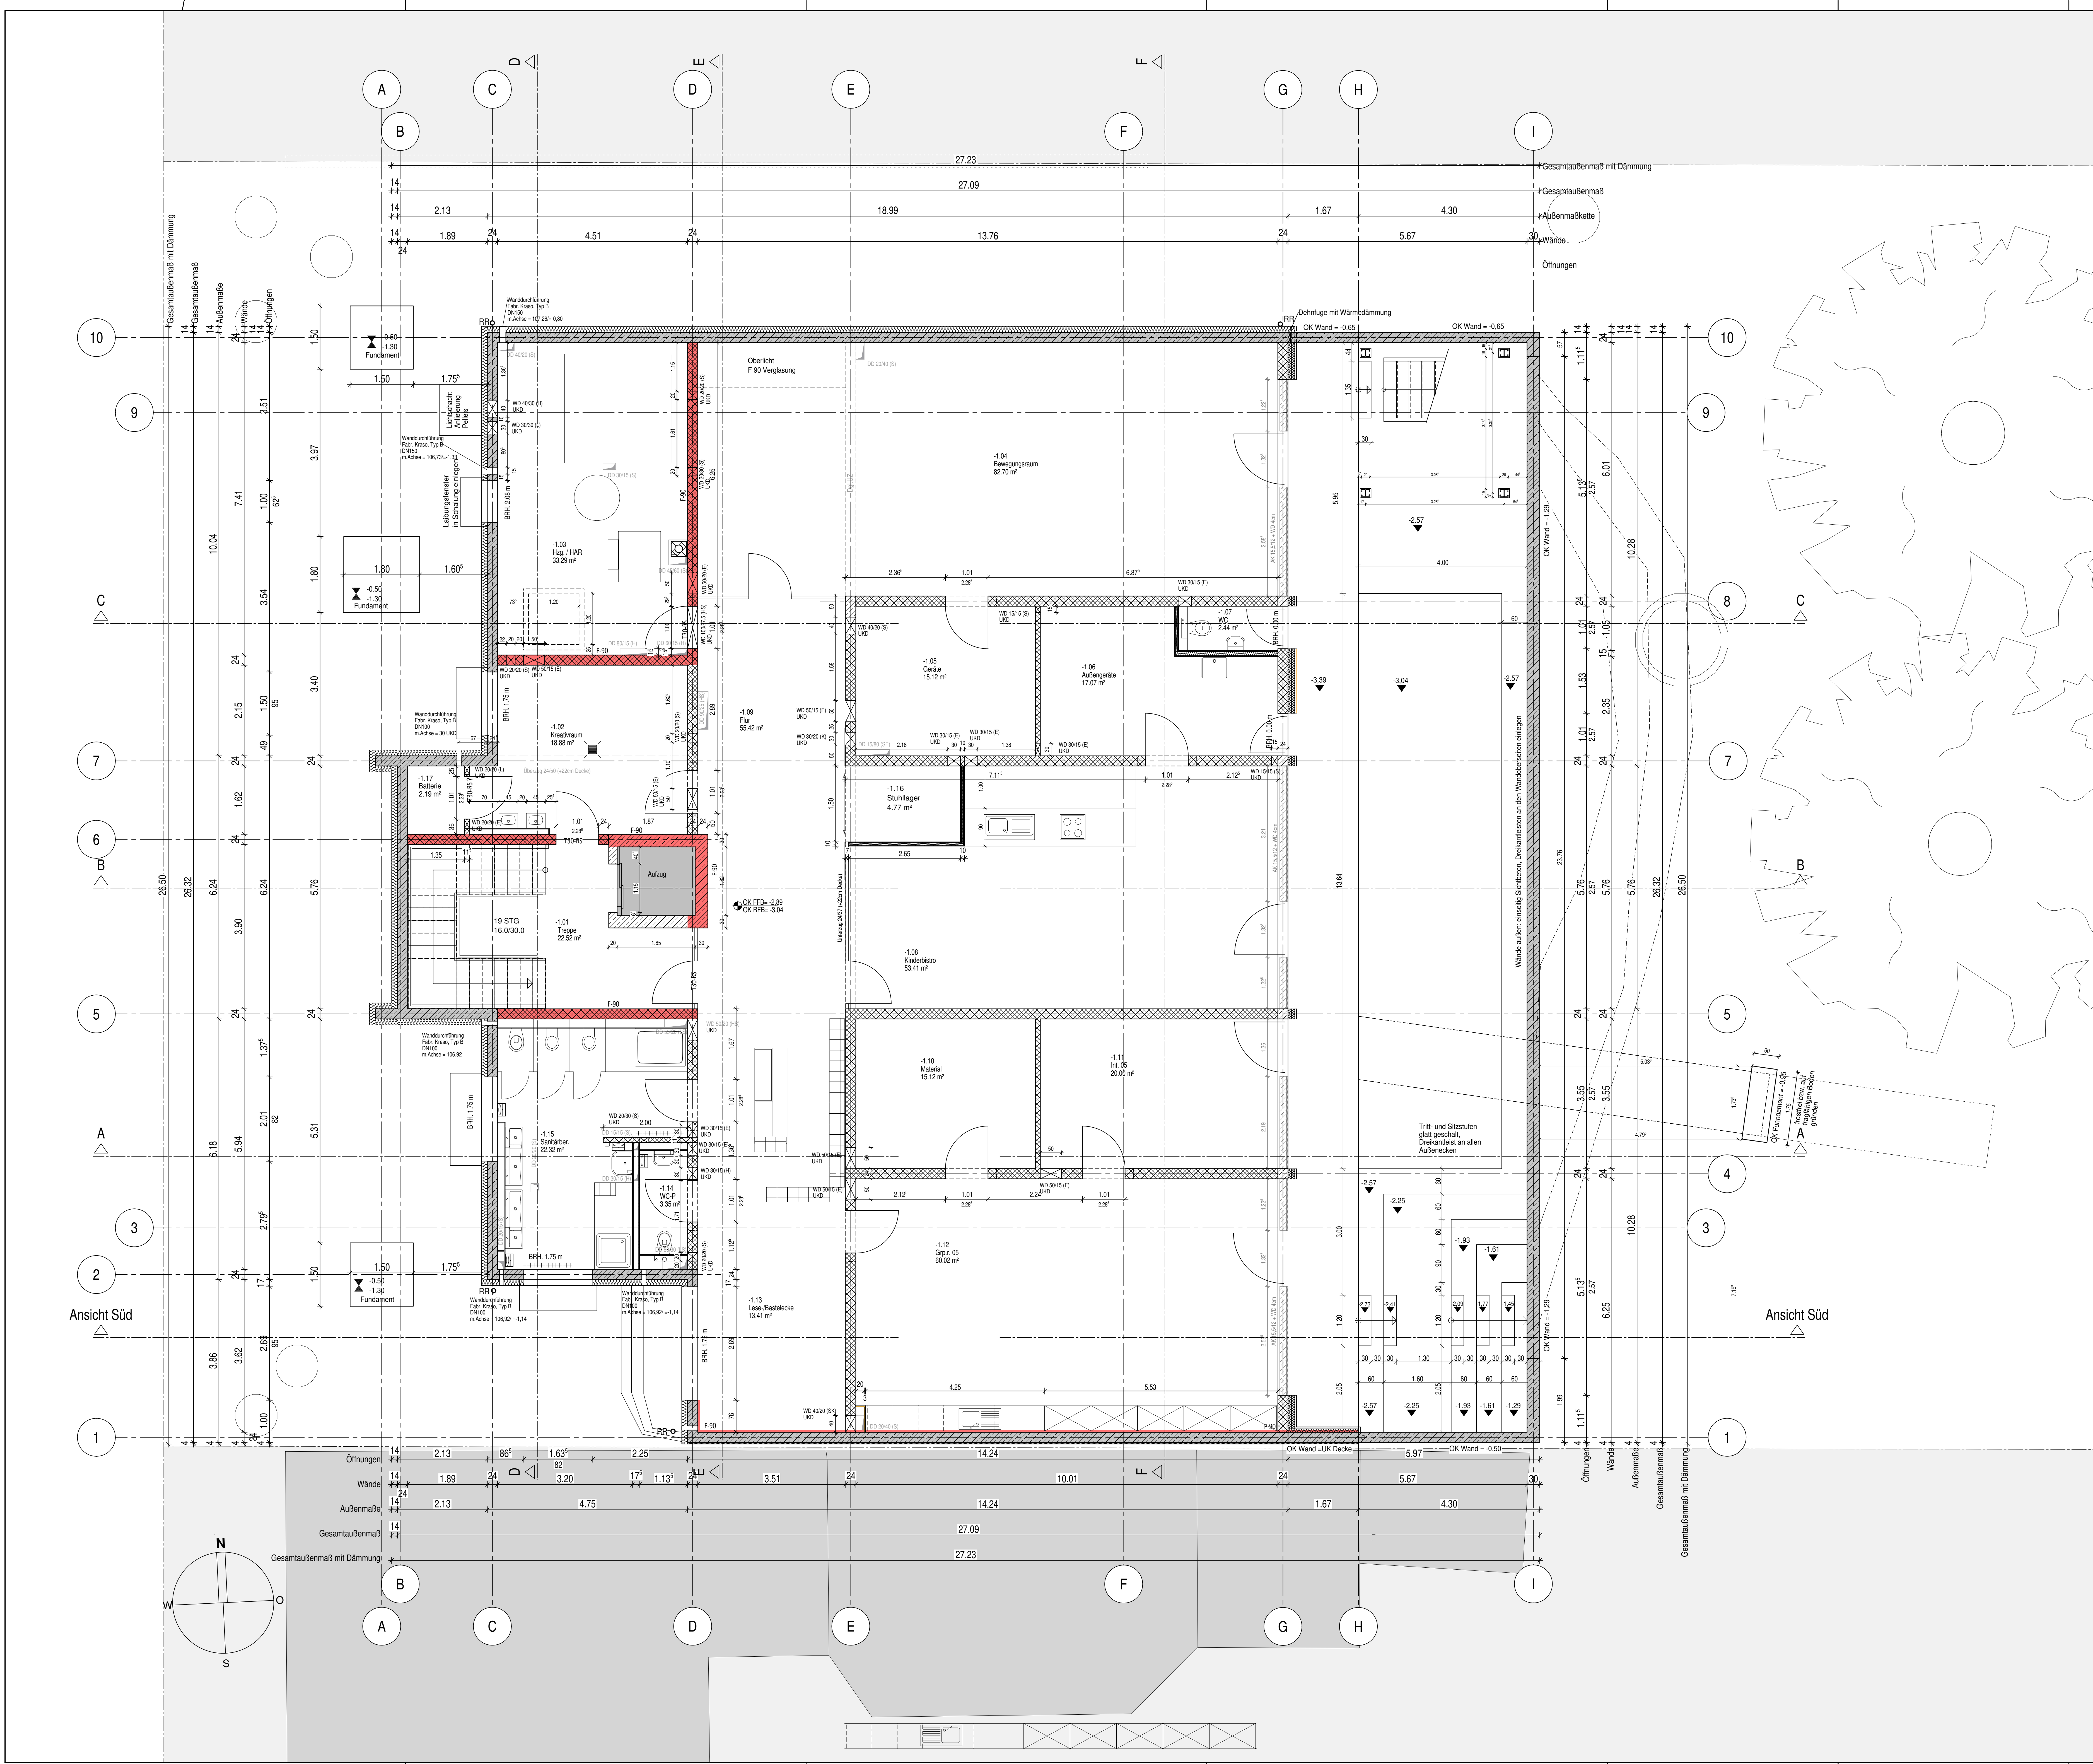

Deckendurchbrüche
siehe auch Deckenpläne.

Bei Öffnungen mit Aufkantung bezieht sich die
Öffnungshöhe auf den Rohfußboden!

Alle Höhenangaben beziehen sich auf EG Rohfußboden.
EG RFB = ± 0,00 entspricht 108,06 ü.NN.

Alle Maße am Bau sind eigenverantwortlich zu prüfen.
Abweichungen sind unverzüglich der Bauleitung zu melden.

- Legende:**
- KS Mauerwerk 20 2.0 DBM
 - Ortbeton C25/30 WU
 - Ortbeton C25/30
 - F-90 feuerbeständig
 - F-30 feuerhemmend

C	CR	Wand- und Deckendurchbrüche geändert	20.05.2019
A	CR	Wand- und Deckendurchbrüche geändert	16.05.2019
Index	Gez.	Änderung / Ergänzung	Datum

WD	Wanddurchbruch	UKD	Unterkernte Decke	KD	Kanaldeckel
DD	Deckendurchbruch	NN	Nähe über Normalnull	KS	Kanalsteine
BD	Böschungsbereich	RA	Rohr- und Abwasser	HKS	Hausklimaschicht
SWS	Senkrechter Wandschnitt	DN	DN	AW	Abwasser
UK	Unterkernte	GR	Gründungsgruppe	W	Wasser
VK	Vorderkernte	GR	Gründungsgruppe	FR	Fahrrad
OK	Obenkernte	GR	Gründungsgruppe	RI	Regenrinne
BRH	Brüstungshöhe	WD	Wanddurchbruch	RO	Reinigungsöffnung
FBS	Fertigfußboden	WLG	Wärmeleitgruppe	TSO	Trittschalldämmung
RFB	Rohfußboden				

Projektnummer:

440

Planstand:

WERKPLANUNG

Maßstab:

1:50

Datum:

13.05.2019

Format:

DIN A0

Gez.:

UL/CR

Plan Nr.:

440 WP 001B

Planverfasser:

Udo Lindenfelser

Bauvorhaben:

Kindergarten St. Franziskus
Stefanienstraße 7, Flst.Nr. 268/6
76709 Kronau

Bauherr:

Seelsorgeeinheit Bad Schönborn- Kronau
Pfarrer Wolfgang Kesenheimer
Kirrlacher Straße 4, 76709 Kronau

Bauteil / Bereich:

Grundriss
Untergeschoss

Telefon:

07257 / 930524

Telefax:

07257 / 930525

mail:

info@ a-u-l.de

www. a-u-l.de