


KD=108.08 ± +0.02
KS=106.22 ± -1.84
©

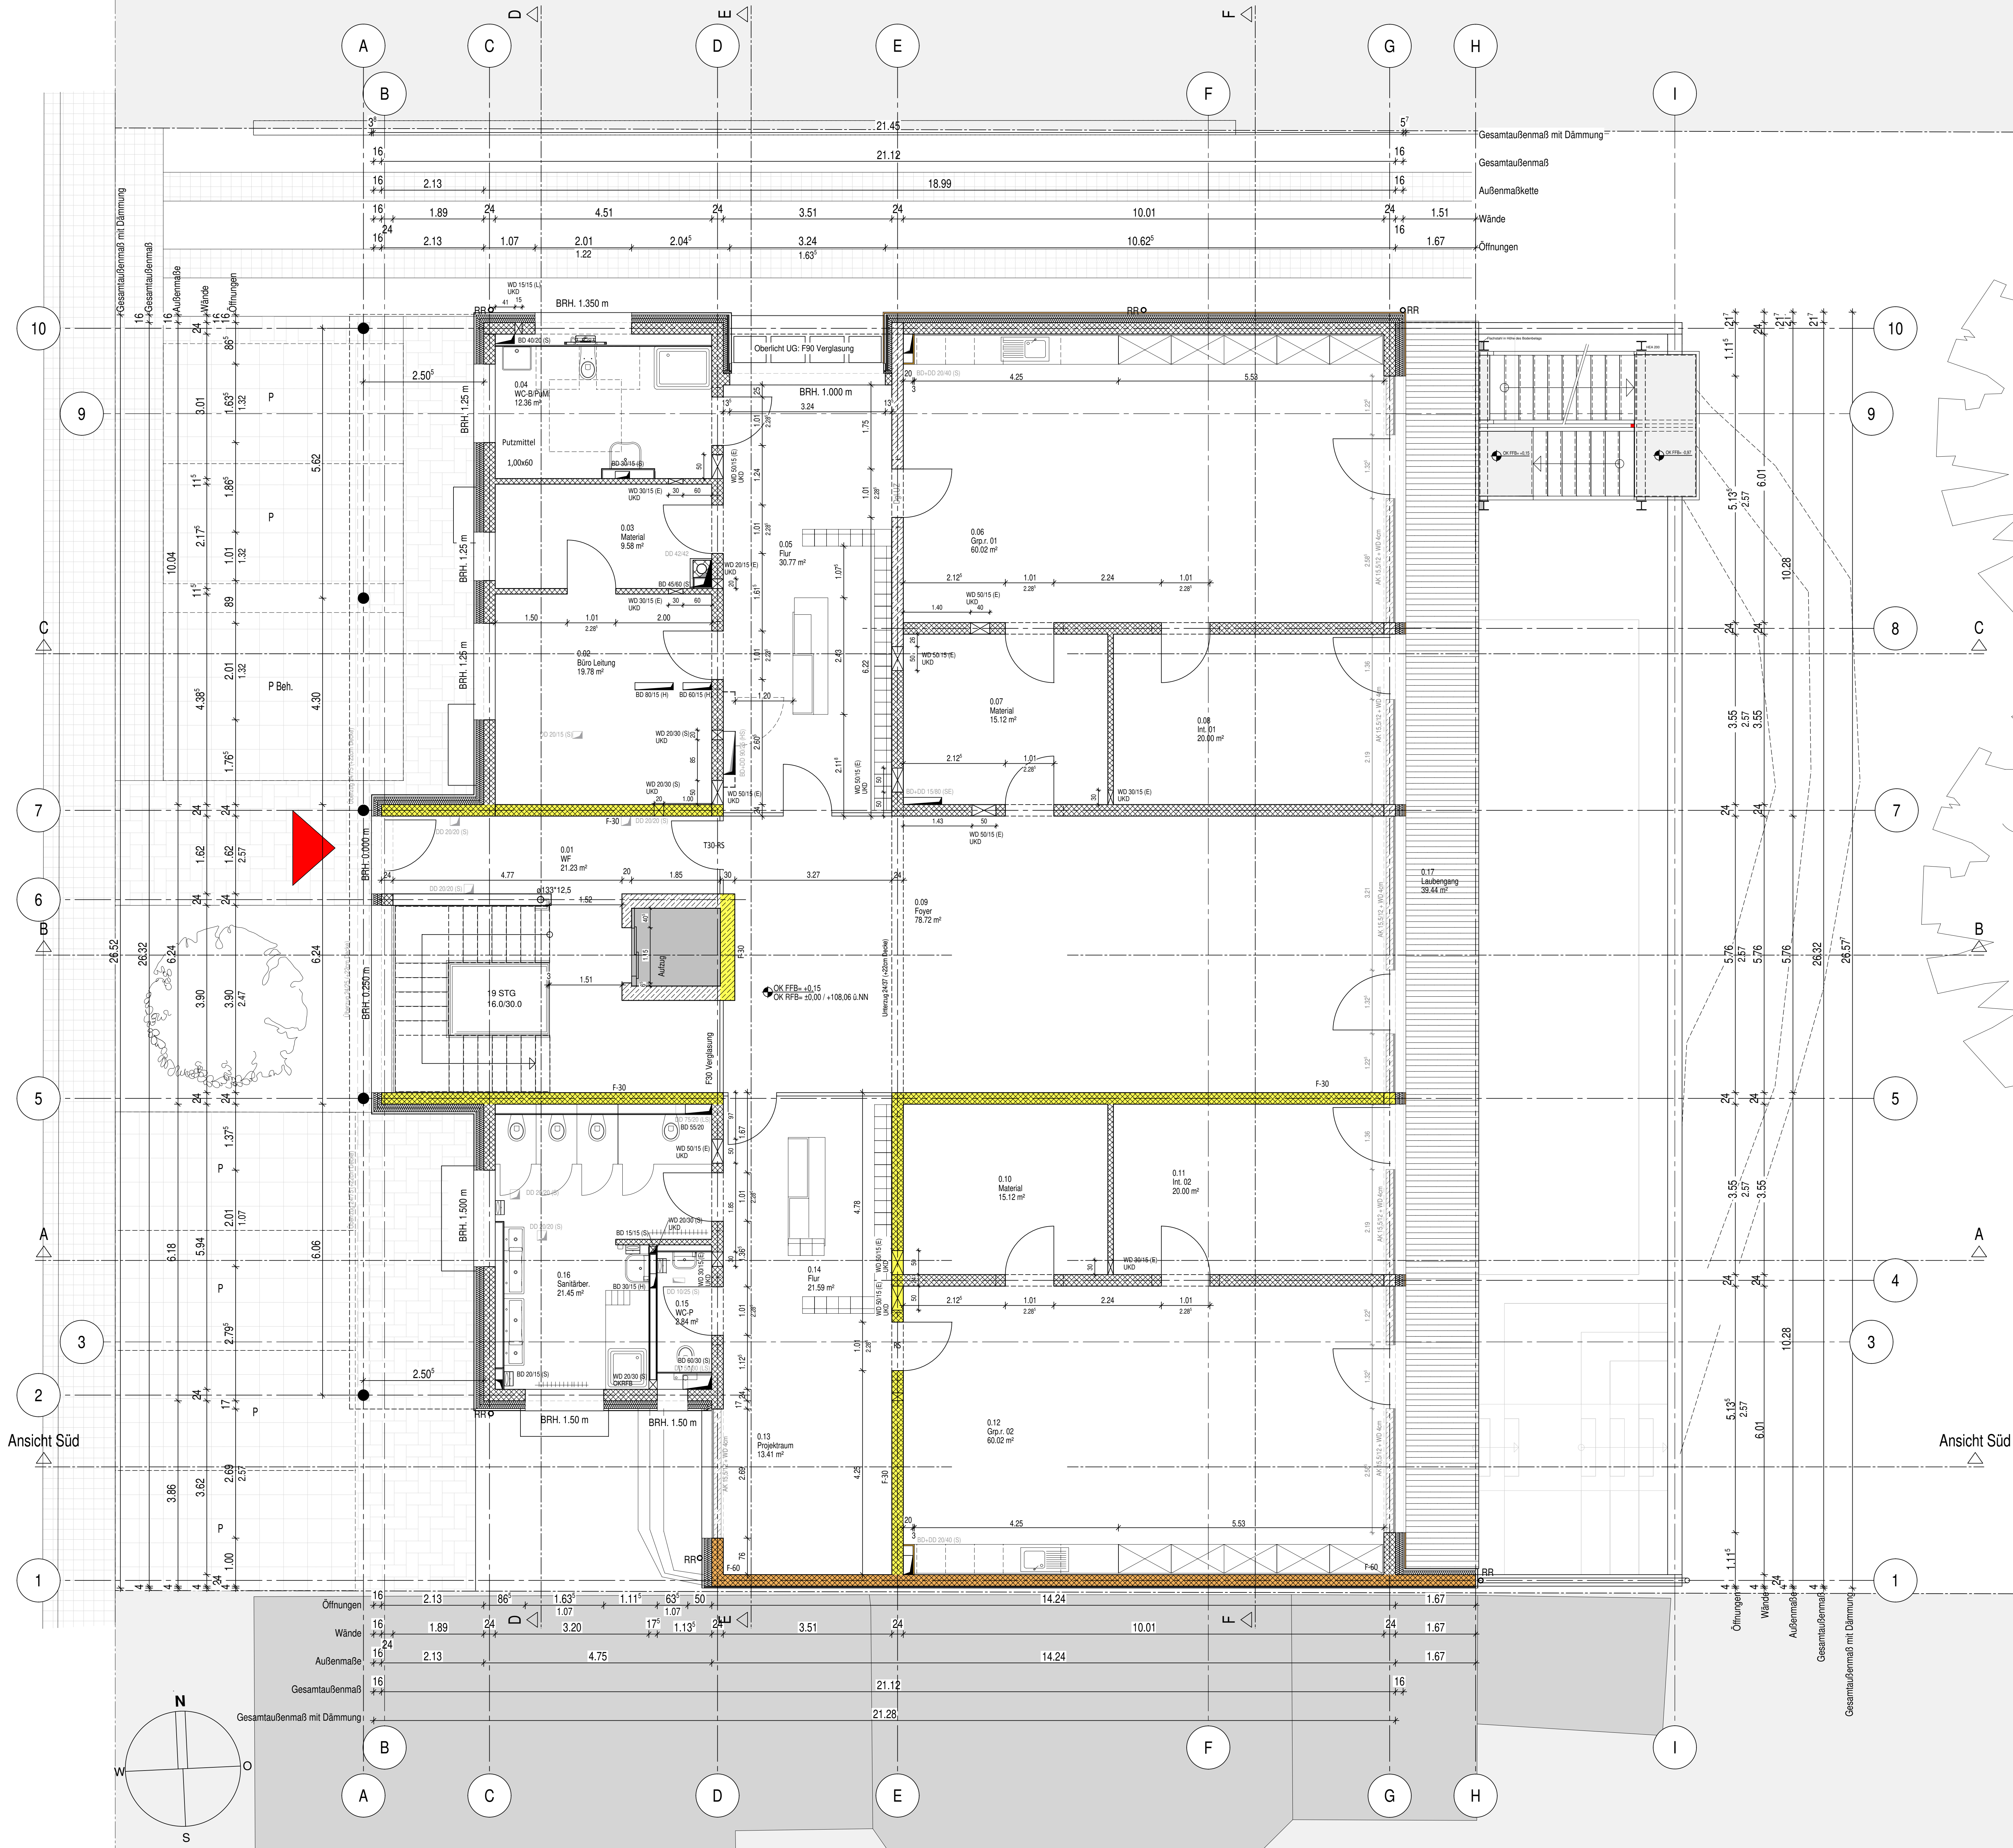

Deckendurchbrüche
siehe auch Deckenpläne.

Bei Öffnungen mit Aufkantung bezieht sich die
Öffnungshöhe auf den Rohfußboden!

Alle Höhenangaben beziehen sich auf EG Rohfußboden.
EG RFB = ± 0,00 entspricht 108,06 ü.NN.

Alle Maße am Bau sind eigenverantwortlich zu prüfen.
Abweichungen sind unverzüglich der Bauleitung zu melden.

Legende:

- KS Mauerwerk 20 2.0 DBM
- Ortbeton C25/30 WU
- Ortbeton C25/30
- F-90 feuerbeständig
- F-60 hochfeuerhemmend
- F-30 feuerhemmend

C	CR	Wanddurchbrüche geändert	21.05.2019
A	CR	Wand- und Deckendurchbrüche geändert	20.05.2019
Index	Gez.	Änderung / Ergänzung	Datum

WD	Wanddurchbruch	UKD	Unterplatte Decke	KD	Kanaldeckel
BD	Bodendurchbruch	NH	Nische	KS	Kanalschacht
SWS	Senkrechter Wandschutz	FBA	Fußbodenauflage	KES	Kanalschacht
UK	Unterplatte	DN	DN	AW	Abwasser
VK	Vorderplatte	RA	Rauchschuttschicht	W	Wasser
OK	Oberrampe	GR	Gründungsplatte	RR	Rohr
BRH	Brüstungshöhe	WD	Wand	RO	Rohr
FBB	Fußboden	WLG	Wärmedämmung	TR	Trennschicht
RFB	Rohfußboden				

Projektnummer: 440	
Planstand: WERKPLANUNG	
Maßstab: 1:50	Bauvorhaben: Kindergarten St. Franziskus Stefanienstraße 7, Flst.Nr. 268/6 76709 Kronau
Datum: 16.05.2019	
Format: DIN A0	Bauherr: Seelsorgeeinheit Bad Schönborn - Kronau Pfarrer Wolfgang Kesenheimer Kirrlacher Straße 4, 76709 Kronau
Gez.: UL/CR	
Plan Nr.: 440 WP 002B	Bauart / Bereich: Grundriss Erdgeschoss

Planverfasser:
Udo Lindenfelser
Dipl.Ing. (FH), Freier Architekt
Energieberater (BAFA)
Beilwegweg 9, 76646 Bruchsal
Telefon: 07257 / 930524
Telefax: 07257 / 930525
mail: info@ a-u-l.de

www. a-u-l.de